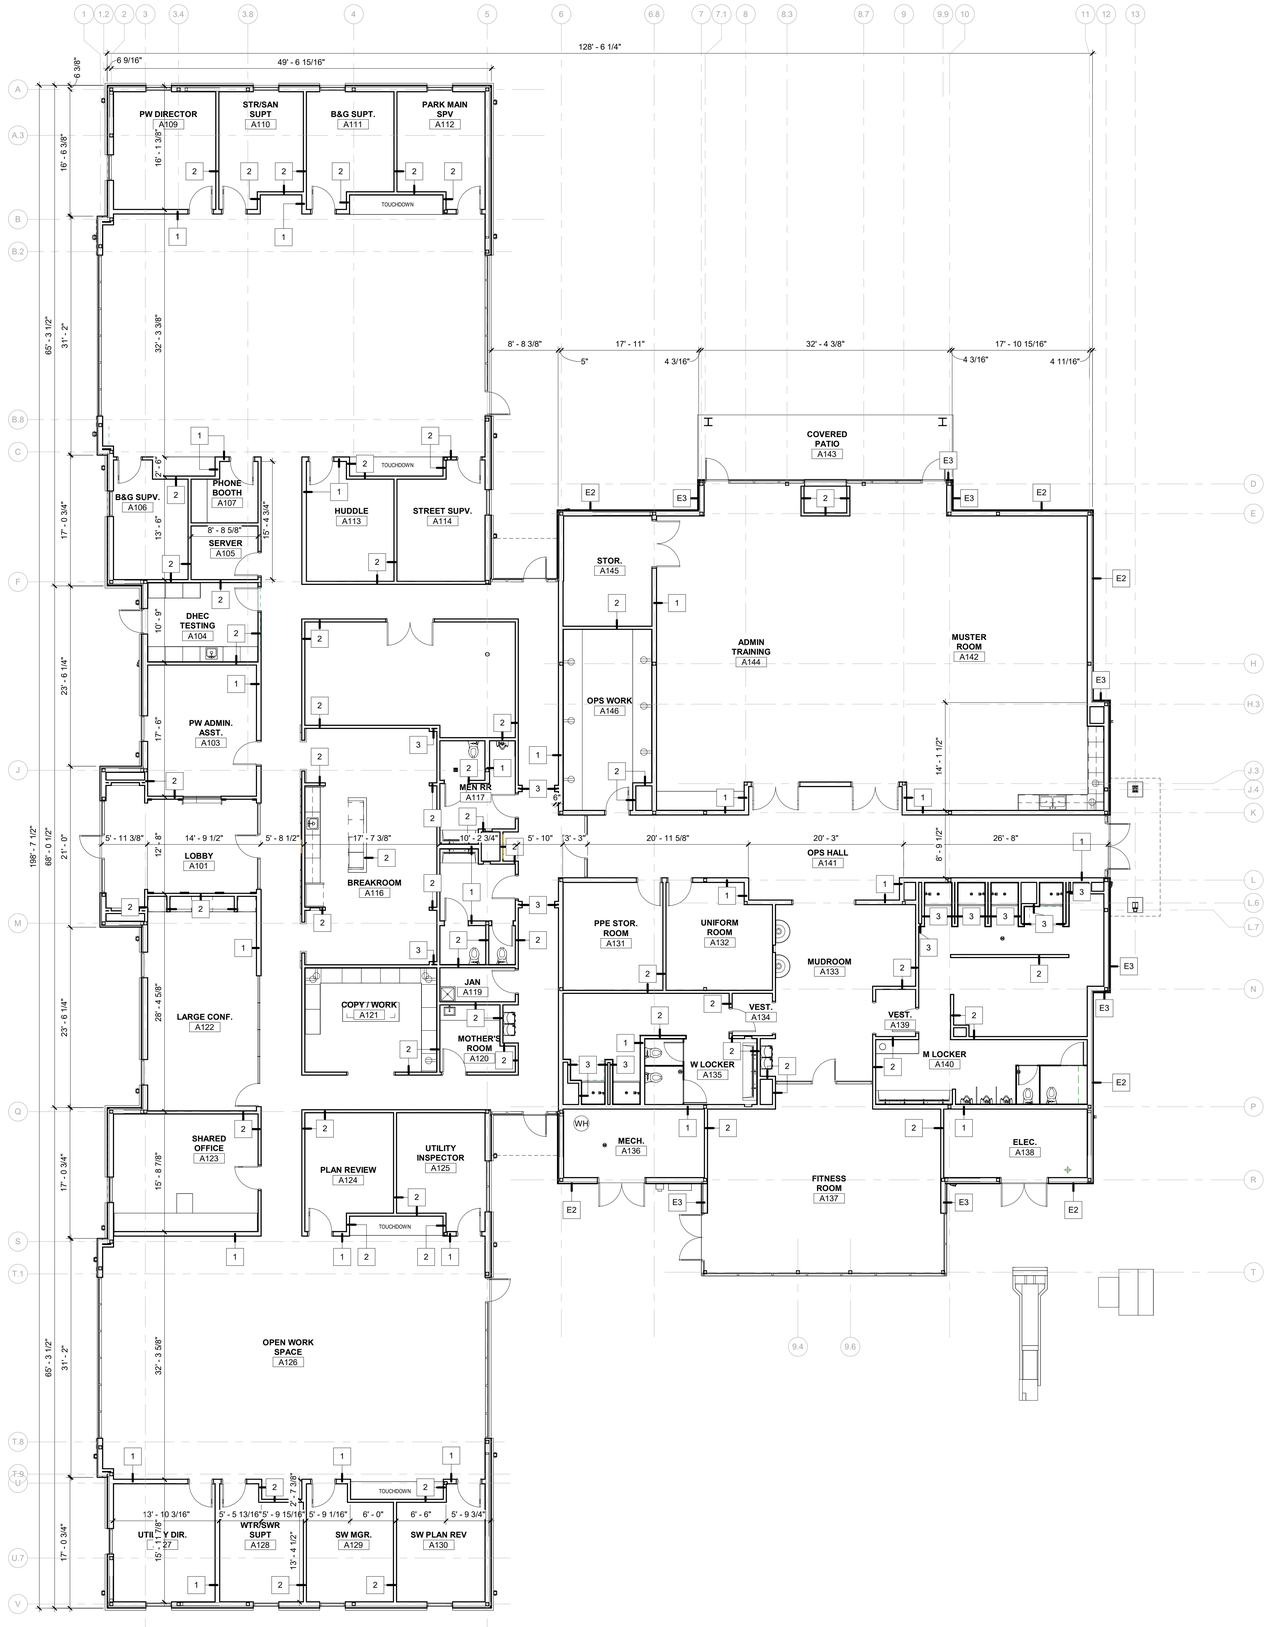

1 A1.01A DIMENSION FLOOR PLAN
1/8" = 1'-0"

GENERAL DIMENSION PLAN NOTES

A. GENERAL CONTRACTOR TO FIELD VERIFY ALL DIMENSIONS AND REPORT DISCREPANCIES IMMEDIATELY TO THE ARCHITECT.

B. DIMENSIONS ARE TO CENTERLINE OF COLUMN LINES, FACE OF INTERIOR STUDS, FACE OF EXTERIOR WALL SHEATHING AND FACE OF MASONRY, UNLESS NOTED OTHERWISE.

C. DOOR JAMBS ARE 6" NEAREST PERPENDICULAR WALL, UNLESS NOTED OTHERWISE.

D. DO NOT SCALE DRAWINGS. USE WRITTEN DIMENSIONS FOR ALL MEASUREMENTS.

WALL TYPE LEGEND

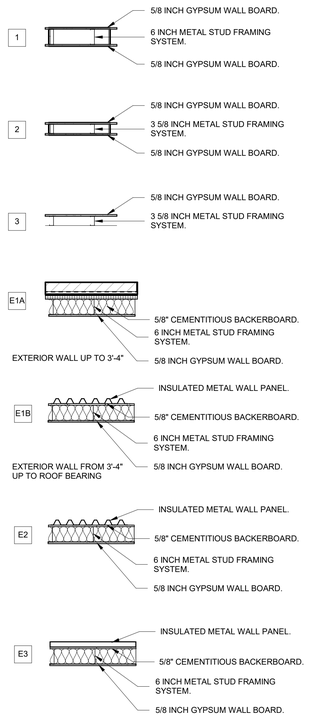

PROJECT NORTH

REFERENCE NORTH

GMC
312 Pendelton Street, Suite C
Rock Hill, SC 29730
T.334.271.3200

Fort Mill SOUTH CAROLINA

DP3 ARCHITECTS

ISSUE	DATE
50% CD	27 JAN 2026
A 100% DD	07/25/2025
B 50% CD COORD	01/15/2026
C 50% CD	01/27/2026

DRAWN BY: KHT
CHECKED BY: MTP

NOT FOR CONSTRUCTION

DIMENSION FLOOR PLAN

ADMINISTRATION BUILDING
2080 BANKS ROAD
FORT MILL, SC 29715
GMC # 24144

A1.01A

1/29/2026 9:21:56 PM